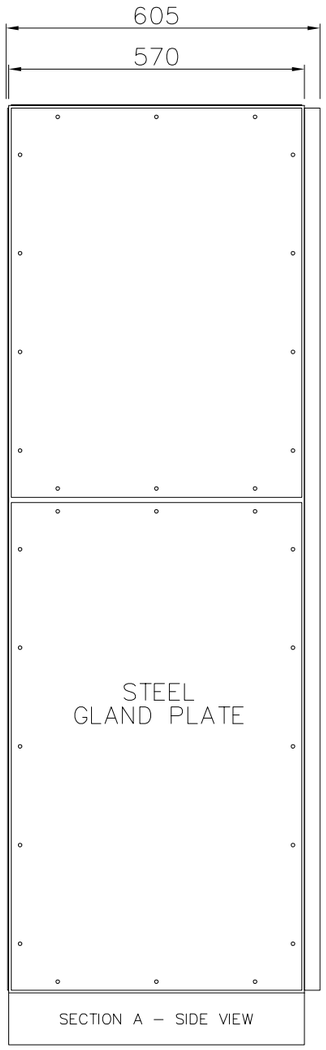

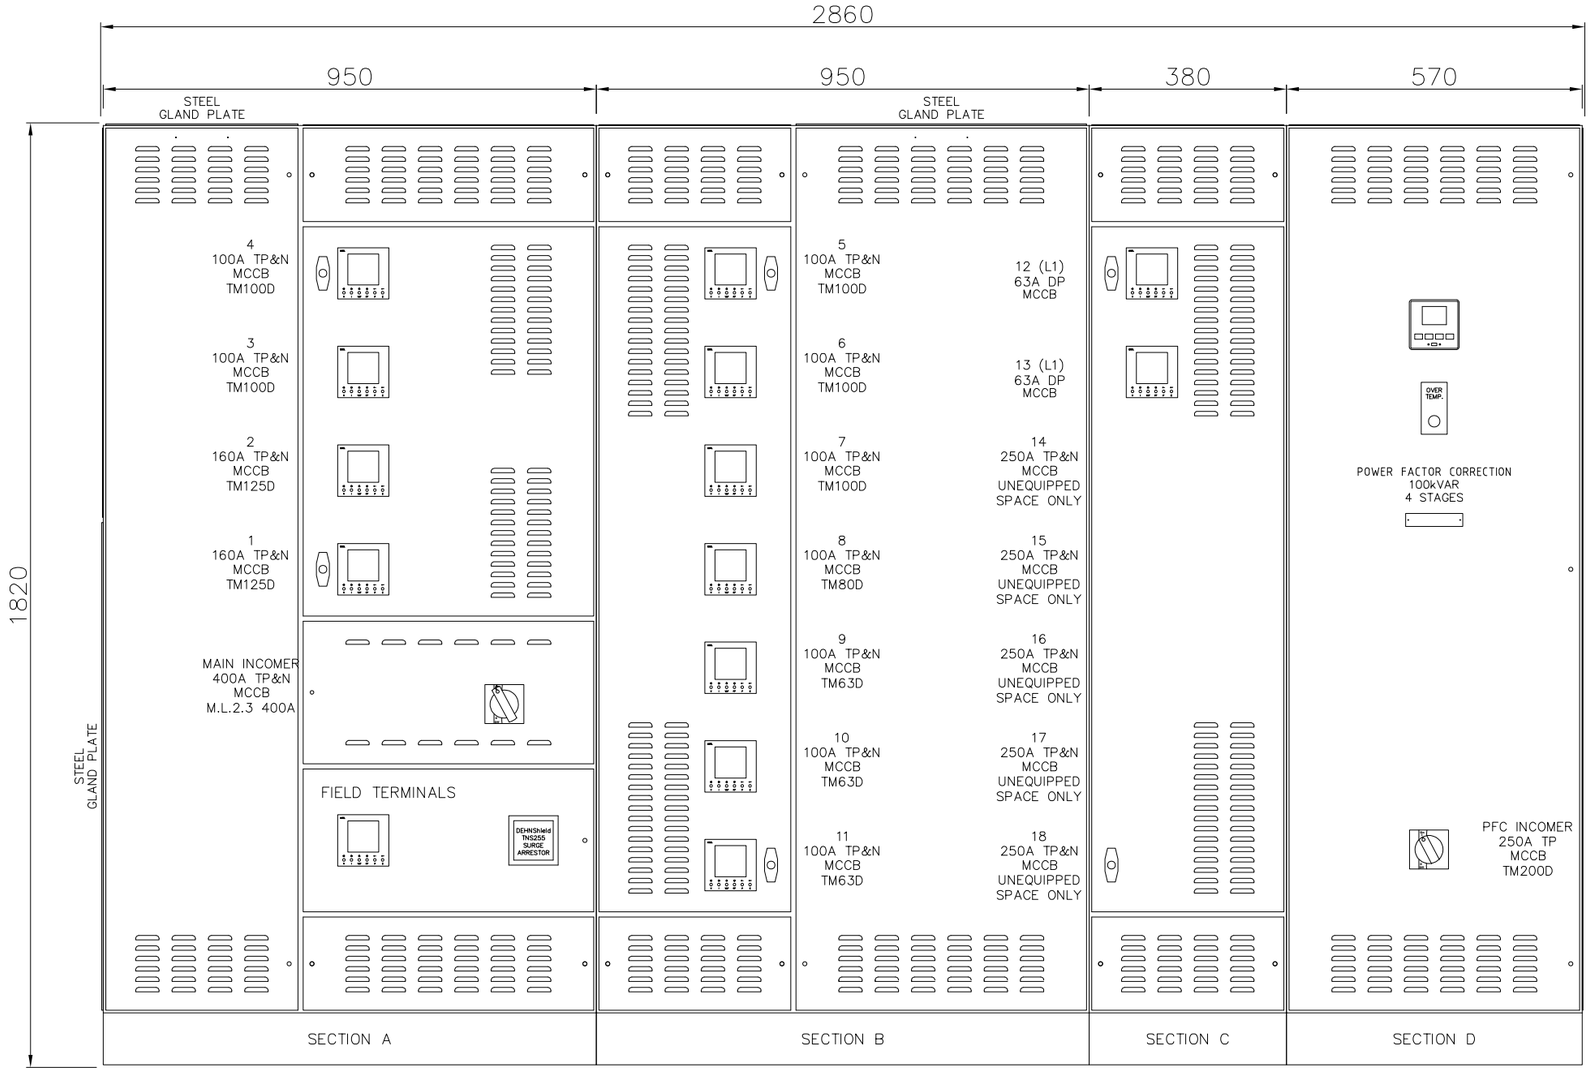

CONSTRUCTION	BS EN 61439-2		
MOUNTING	FLOOR STANDING		
ACCESS	FRONT		
I.P RATING	IP41		
FORM	FORM 4 TYPE 2		
COLOUR	RAL 7035 (LIGHT GREY)		
INCOMING	LHS		
OUTGOING	TOP		
SUPPLY VOLTAGE	400/230V AC 50Hz		
Ui/Uimp	690V/6kV		
Icw	36kA 1 SECOND		
Ipk	80kA		
BUSBAR SYMBOL	BUSBAR SIZE	In	
M	40 x 6mm BOTTOM REAR	630A	
EARTHBAR	40 x 6mm TOP FRONT		

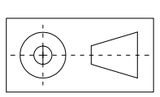

PANEL DEPTH: 630mm
PLINTH DEPTH: 570mm
PLINTH HEIGHT: 100mm

MICHAEL SMITH
SWITCHGEAR
ELECTRICAL DISTRIBUTION & CONTROL
4 ELLAND ROAD, BRAUNSTONE FRITH INDUSTRIAL ESTATE,
LEICESTER, LE3 1TU
TEL: 0116 275 4100
WWW.MSSL.UK.COM INFO@MSSL.UK.COM

CUSTOMER
TEC ELECTRICAL SERVICES LTD

TITLE
KINGSBURY SCHOOL POOL, TAMWORTH
LV SWITCHBOARD

MOD'n	DESCRIPTION	DRAWN	CHECK	DATE
A	TOP CABLE EXIT	S.B	L.B	11-06-25
B				
C				
D				
E				
F				

DRAWN	CHECK	ISSUE	SHEET	DATE	DRAWING No.
S.BROWN	L.B	2	1 OF 3	29-05-25	25803-1

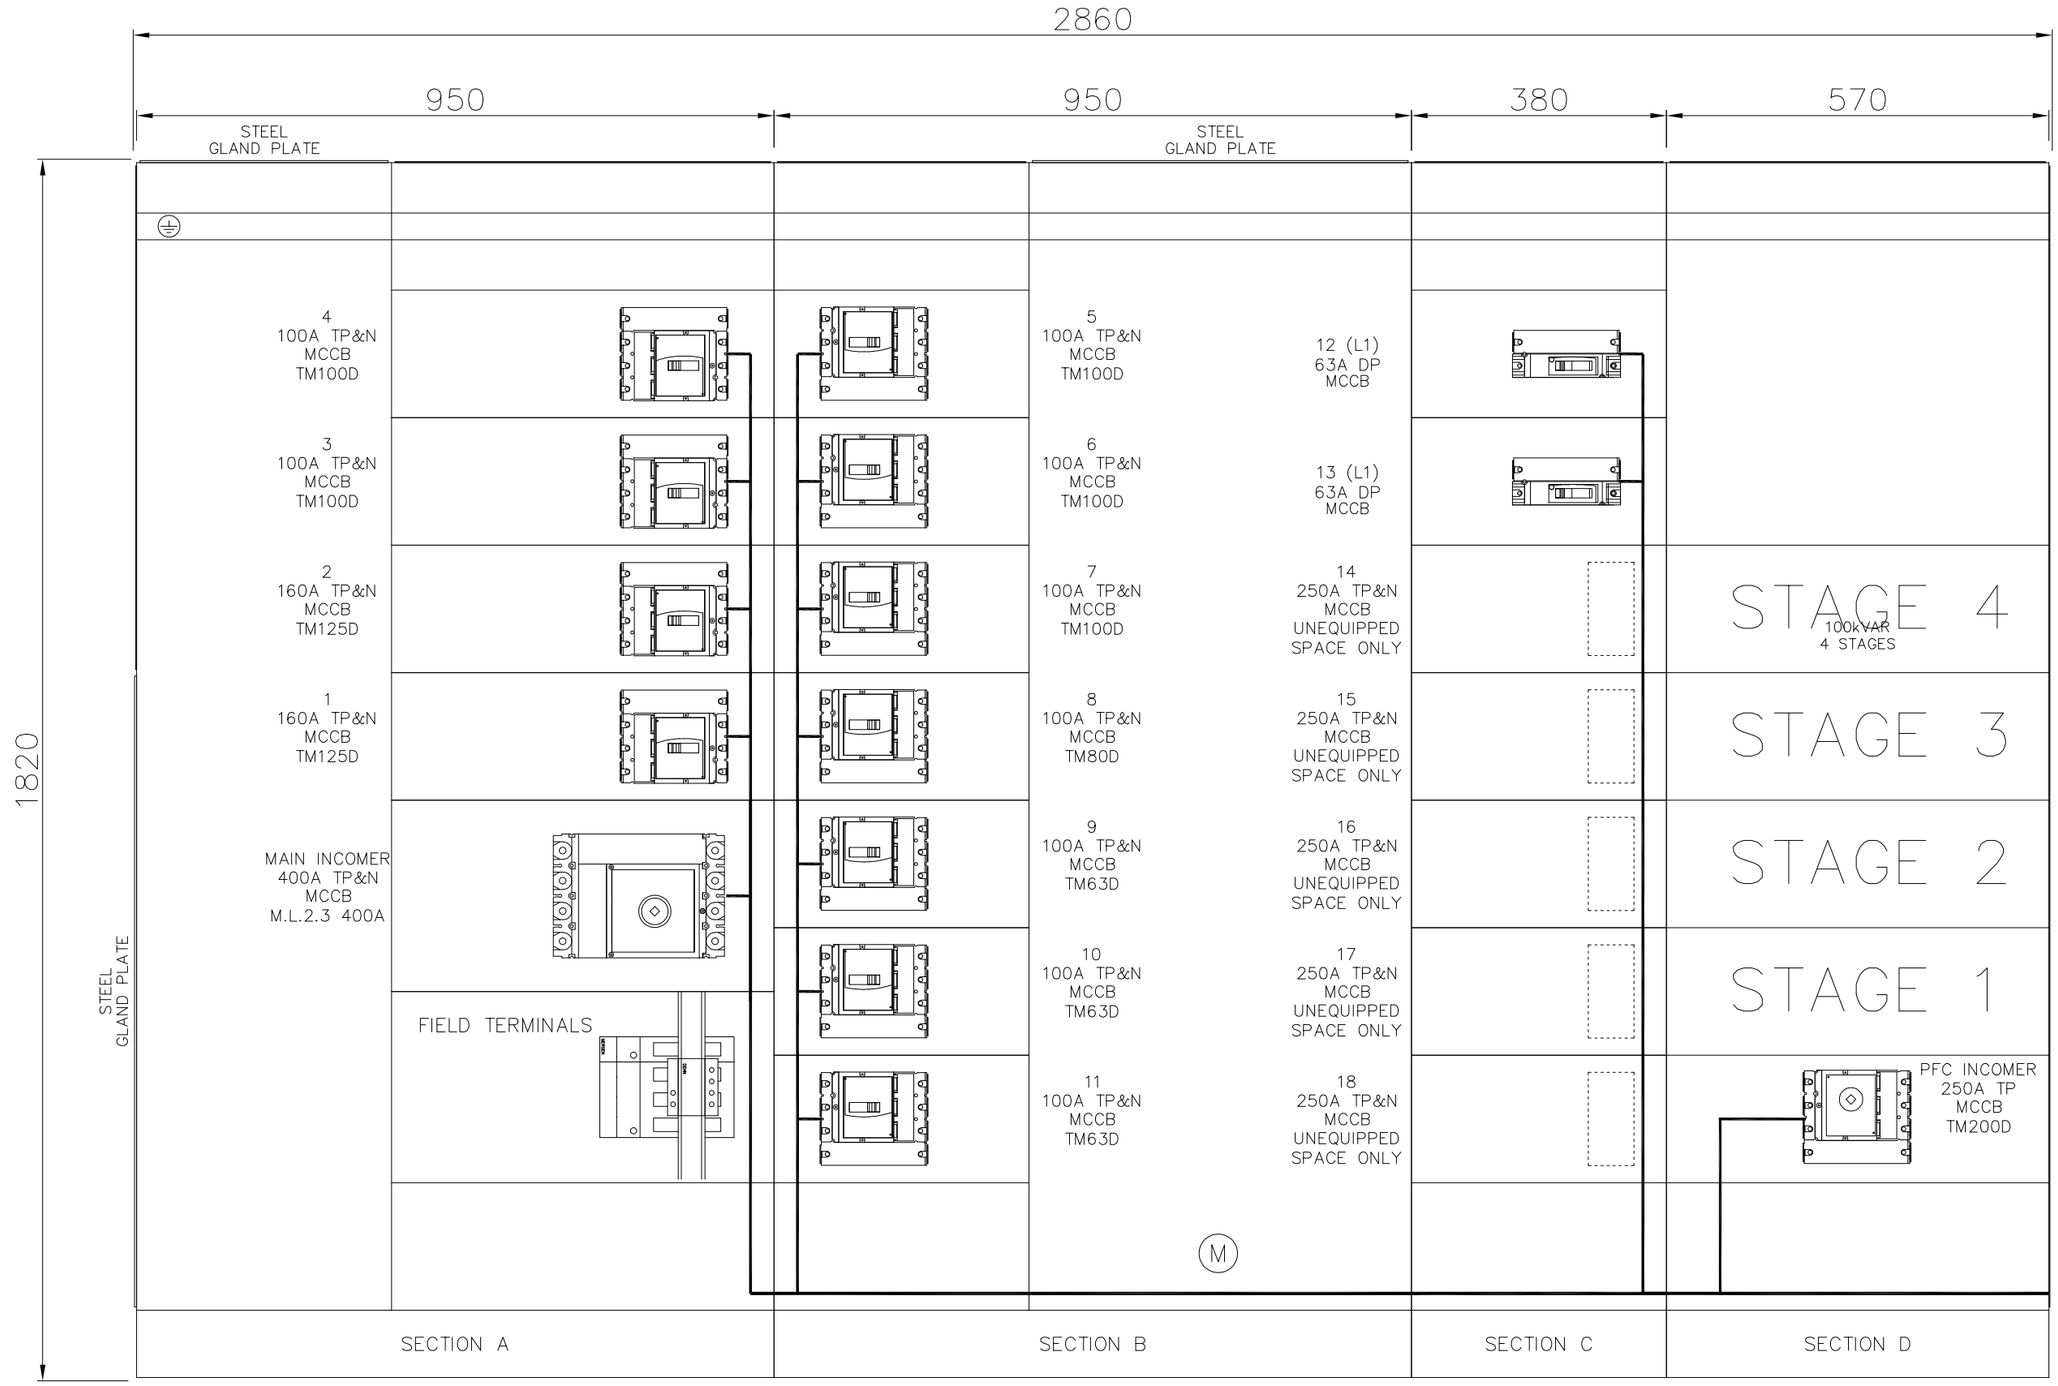

BUSBAR RATING			
Icw		36kA 1 SECOND	
Ipk		80kA	
BUSBAR SYMBOL		BUSBAR SIZE	In
	M	40 x 6mm BOTTOM REAR	630A
	A		
	B		
	C		
	D		
	E		
	F		
EARTHBAR	⏚	40 x 6mm TOP FRONT	

MICHAEL SMITH
SWITCHGEAR
ELECTRICAL DISTRIBUTION & CONTROL
4 ELLAND ROAD, BRAUNSTONE FRITH INDUSTRIAL ESTATE,
LEICESTER, LE3 1TU
TEL: 0116 275 4100
WWW.MSSL.UK.COM INFO@MSSL.UK.COM

CUSTOMER

TEC ELECTRICAL SERVICES LTD

TITLE

KINGSBURY SCHOOL POOL, TAMWORTH
LV SWITCHBOARD

MOD'n	DESCRIPTION	DRAWN	CHECK	DATE
A	TOP CABLE EXIT	S.B	L.B	11-06-25
B				
C				
D				
E				
F				

DRAWN	CHECK	ISSUE	SHEET	DATE	DRAWING No.
S.BROWN	L.B	2	2 OF 3	29-05-25	25803-1

PLAN VIEW

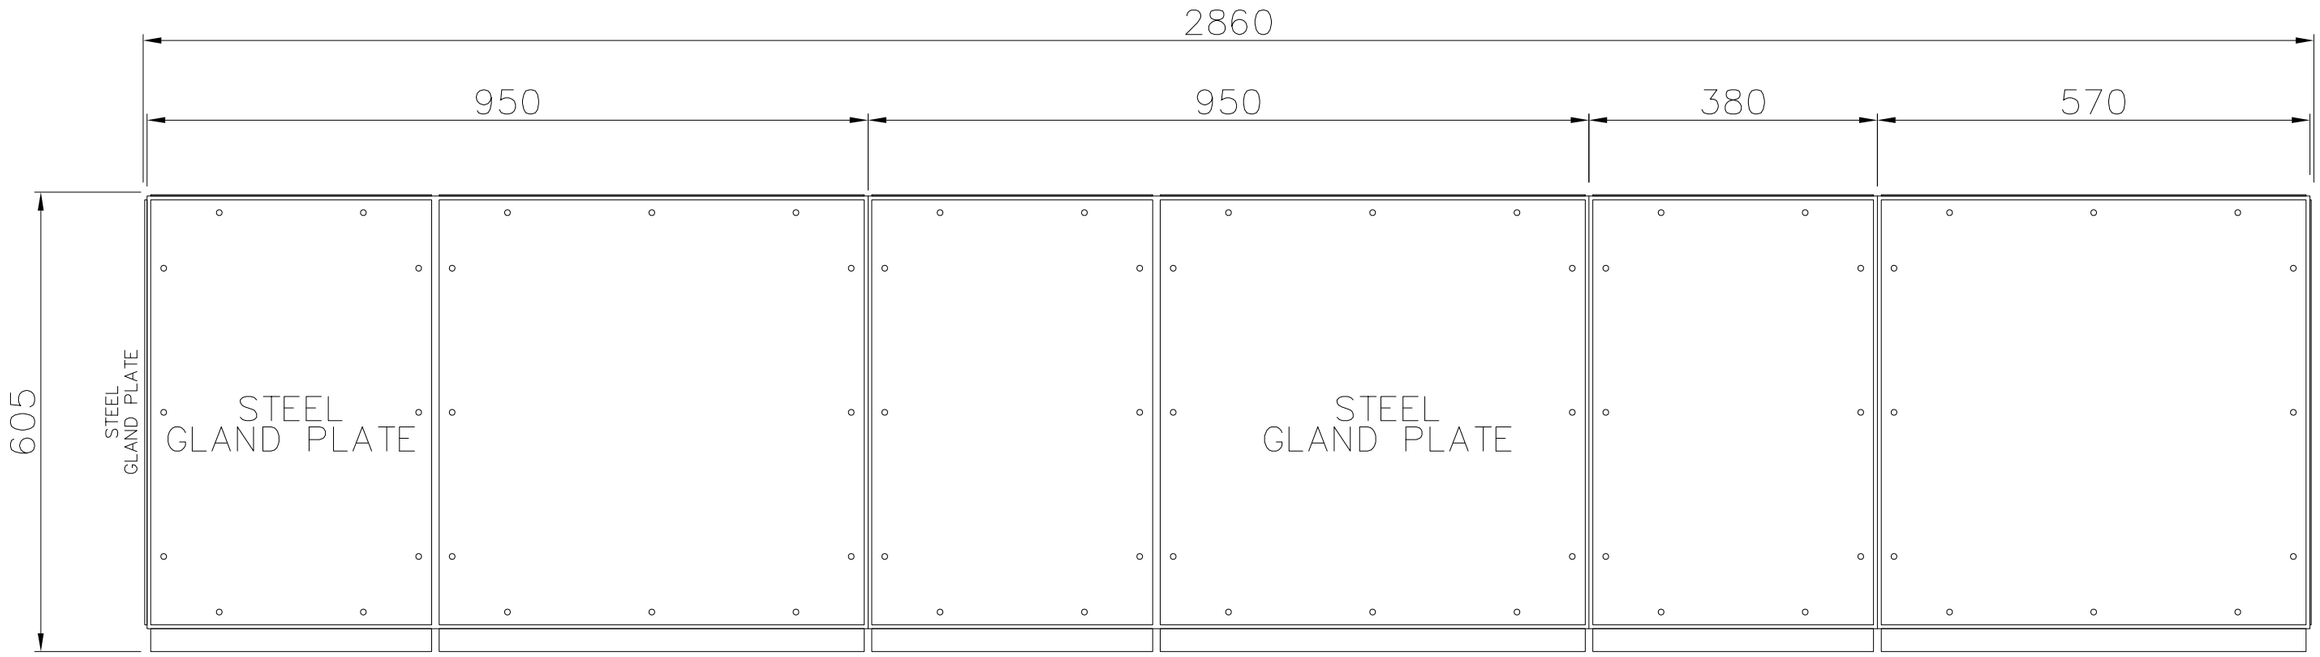

MICHAEL SMITH
SWITCHGEAR
ELECTRICAL DISTRIBUTION & CONTROL
4 ELLAND ROAD, BRAUNSTONE FRITH INDUSTRIAL ESTATE,
LEICESTER, LE3 1TU
TEL: 0116 275 4100
WWW.MSSL.UK.COM INFO@MSSL.UK.COM

CUSTOMER
TEC ELECTRICAL SERVICES LTD

TITLE
KINGSBURY SCHOOL POOL, TAMWORTH
LV SWITCHBOARD

MOD'n	DESCRIPTION	DRAWN	CHECK	DATE
A	TOP CABLE EXIT	S.B	L.B	11-06-25
B				
C				
D				
E				
F				

DRAWN	CHECK	ISSUE	SHEET	DATE	DRAWING No.
S.BROWN	L.B	2	3 OF 3	29-05-25	25803-1