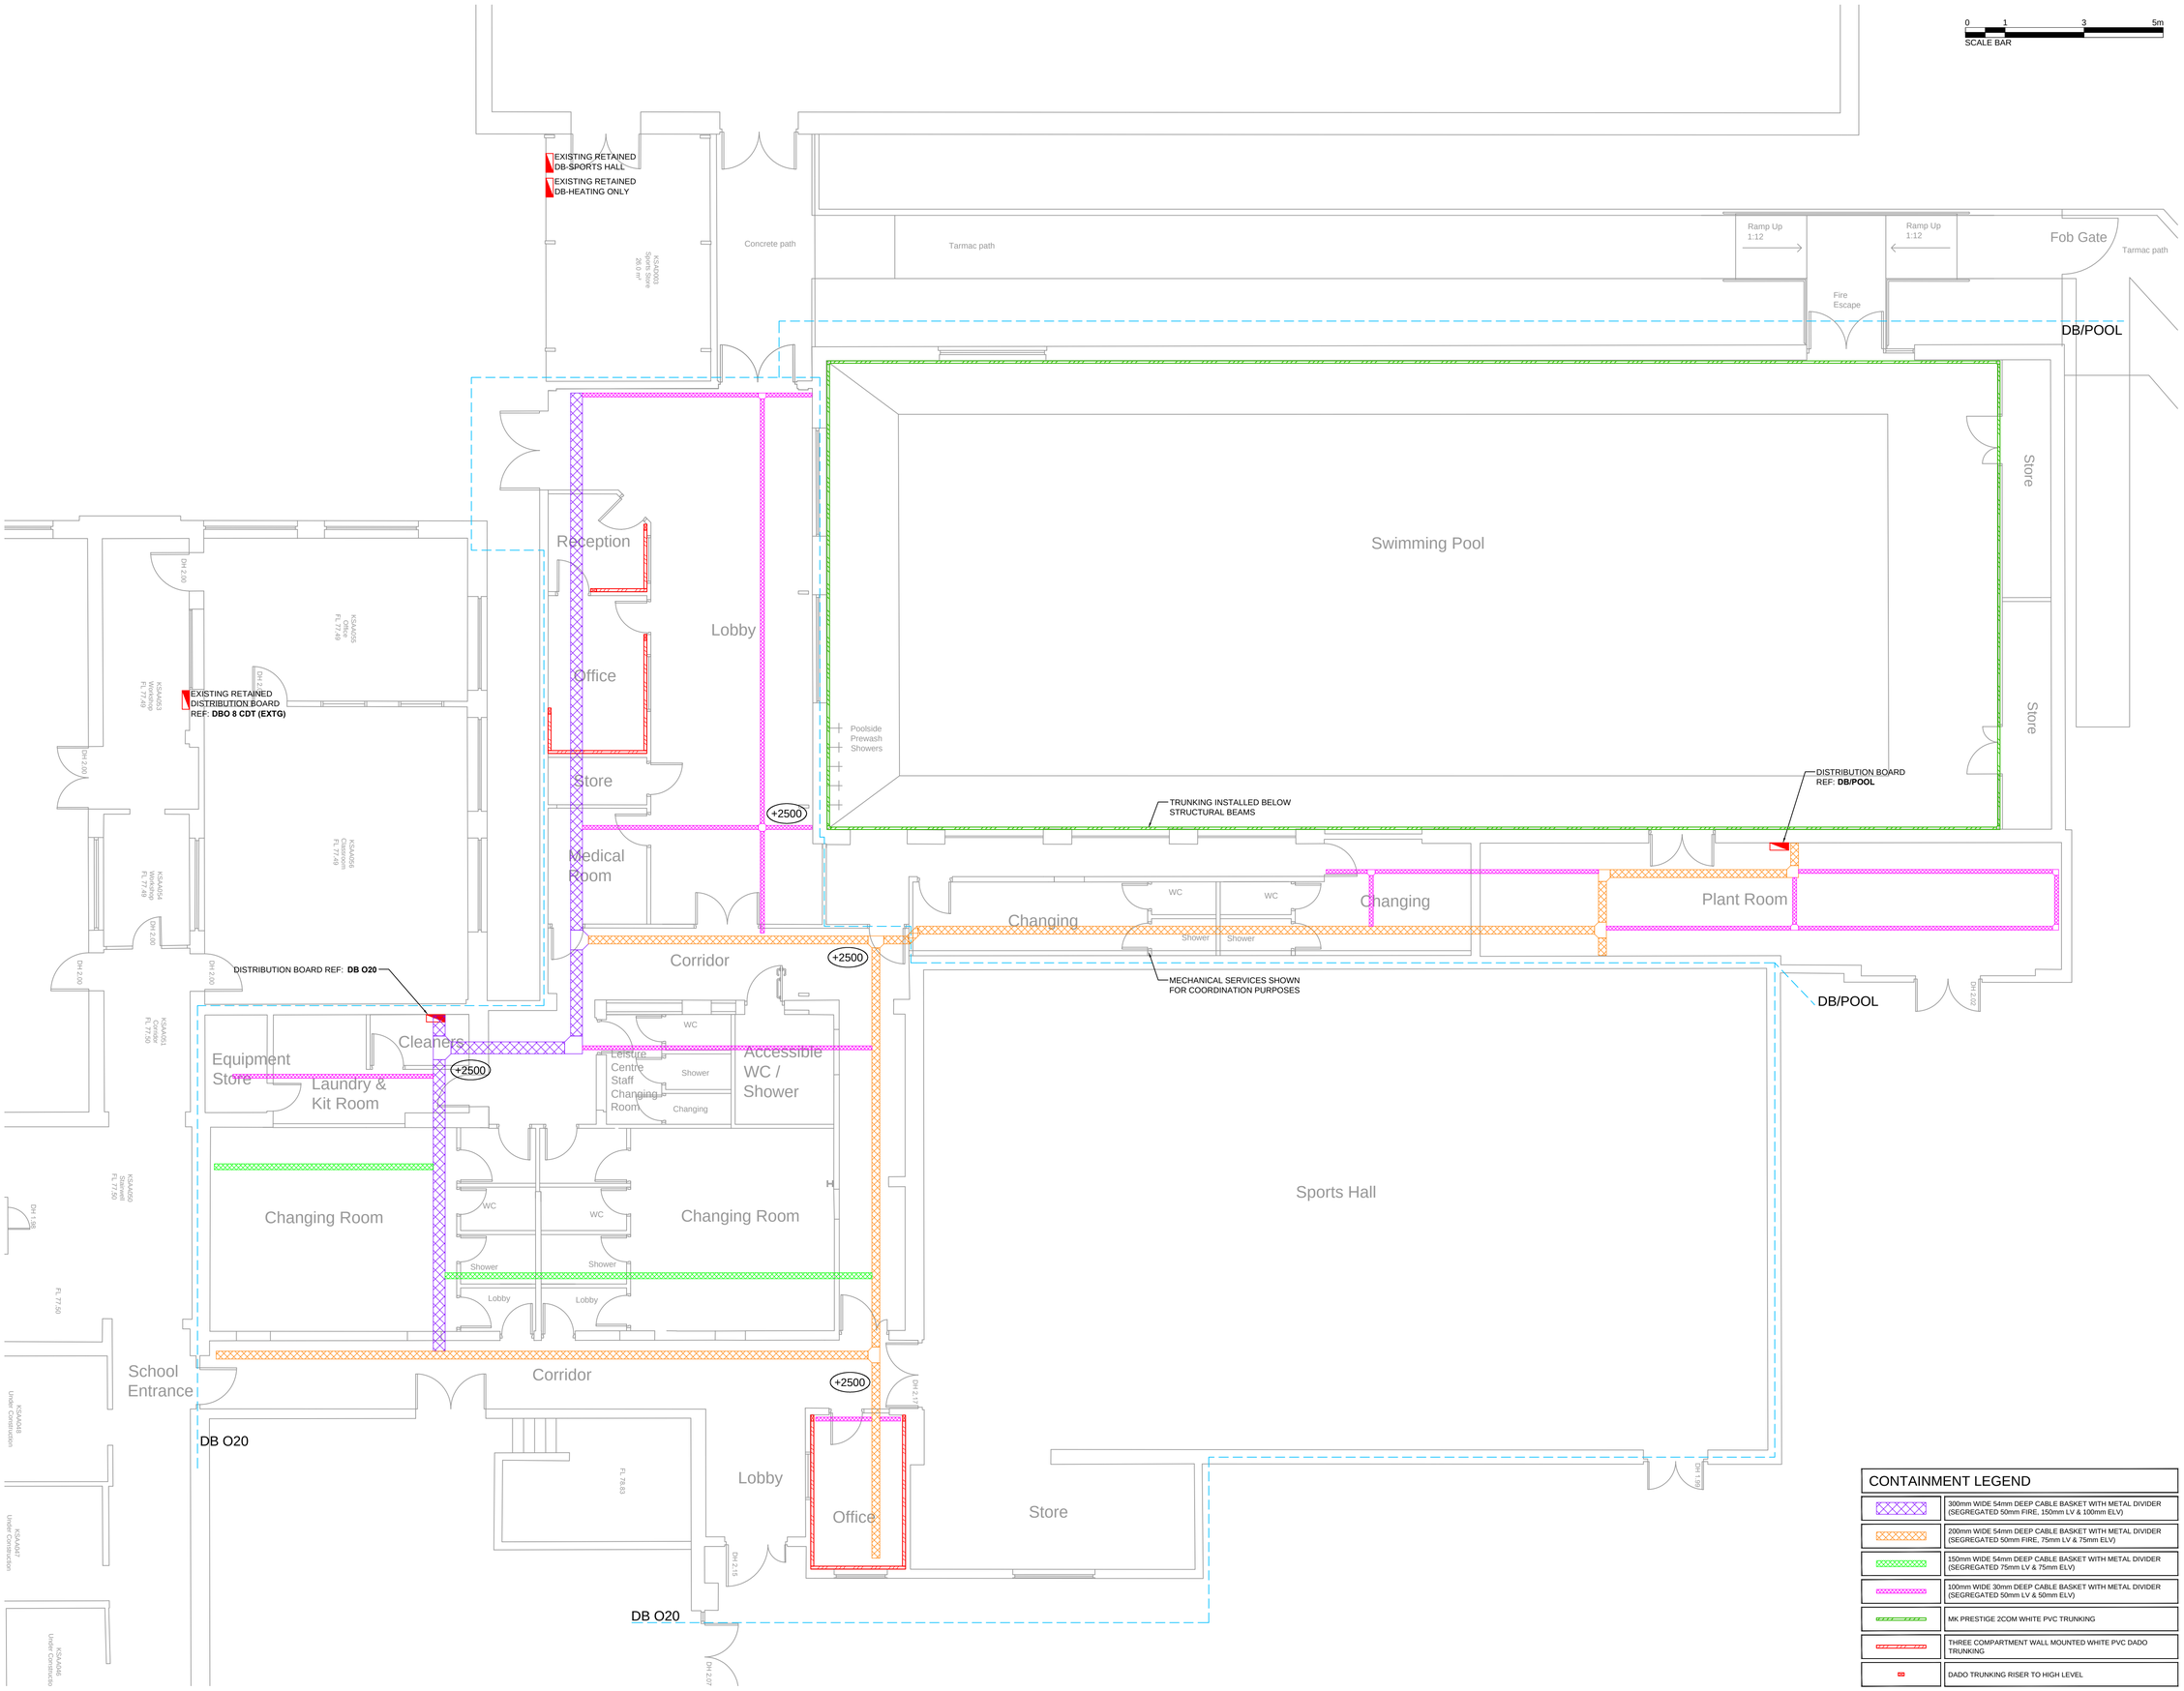

CONTAINMENT LEGEND

	300mm WIDE 54mm DEEP CABLE BASKET WITH METAL DIVIDER (SEGREGATED 50mm FIRE, 150mm LV & 100mm ELV)
	200mm WIDE 54mm DEEP CABLE BASKET WITH METAL DIVIDER (SEGREGATED 50mm FIRE, 75mm LV & 75mm ELV)
	150mm WIDE 54mm DEEP CABLE BASKET WITH METAL DIVIDER (SEGREGATED 75mm LV & 75mm ELV)
	100mm WIDE 30mm DEEP CABLE BASKET WITH METAL DIVIDER (SEGREGATED 50mm LV & 50mm ELV)
	MK PRESTIGE 2COM WHITE PVC TRUNKING
	THREE COMPARTMENT WALL MOUNTED WHITE PVC DADO TRUNKING
	DADO TRUNKING RISER TO HIGH LEVEL

NOTES

ORIGINAL A1

DO NOT SCALE FROM THIS DRAWING.
IF IN DOUBT ASK.

AS FITTED DRAWING

Originator

Tec Electrical Services Ltd

NICEIC APPROVED CONTRACTOR

Client

gleeds

Project

KINGSBURY SCHOOL SWIMMING POOL REFURBISHMENT

Title

CONTAINMENT LAYOUT

Design	Drawn	Date
TEC	TEC	FEB '26

Scale

1:75 @ A1

Background Drawing

NTBS4235 Kingsbury School 01-10-25

Drawing No. E200

Rev AF

Status

AS FITTED