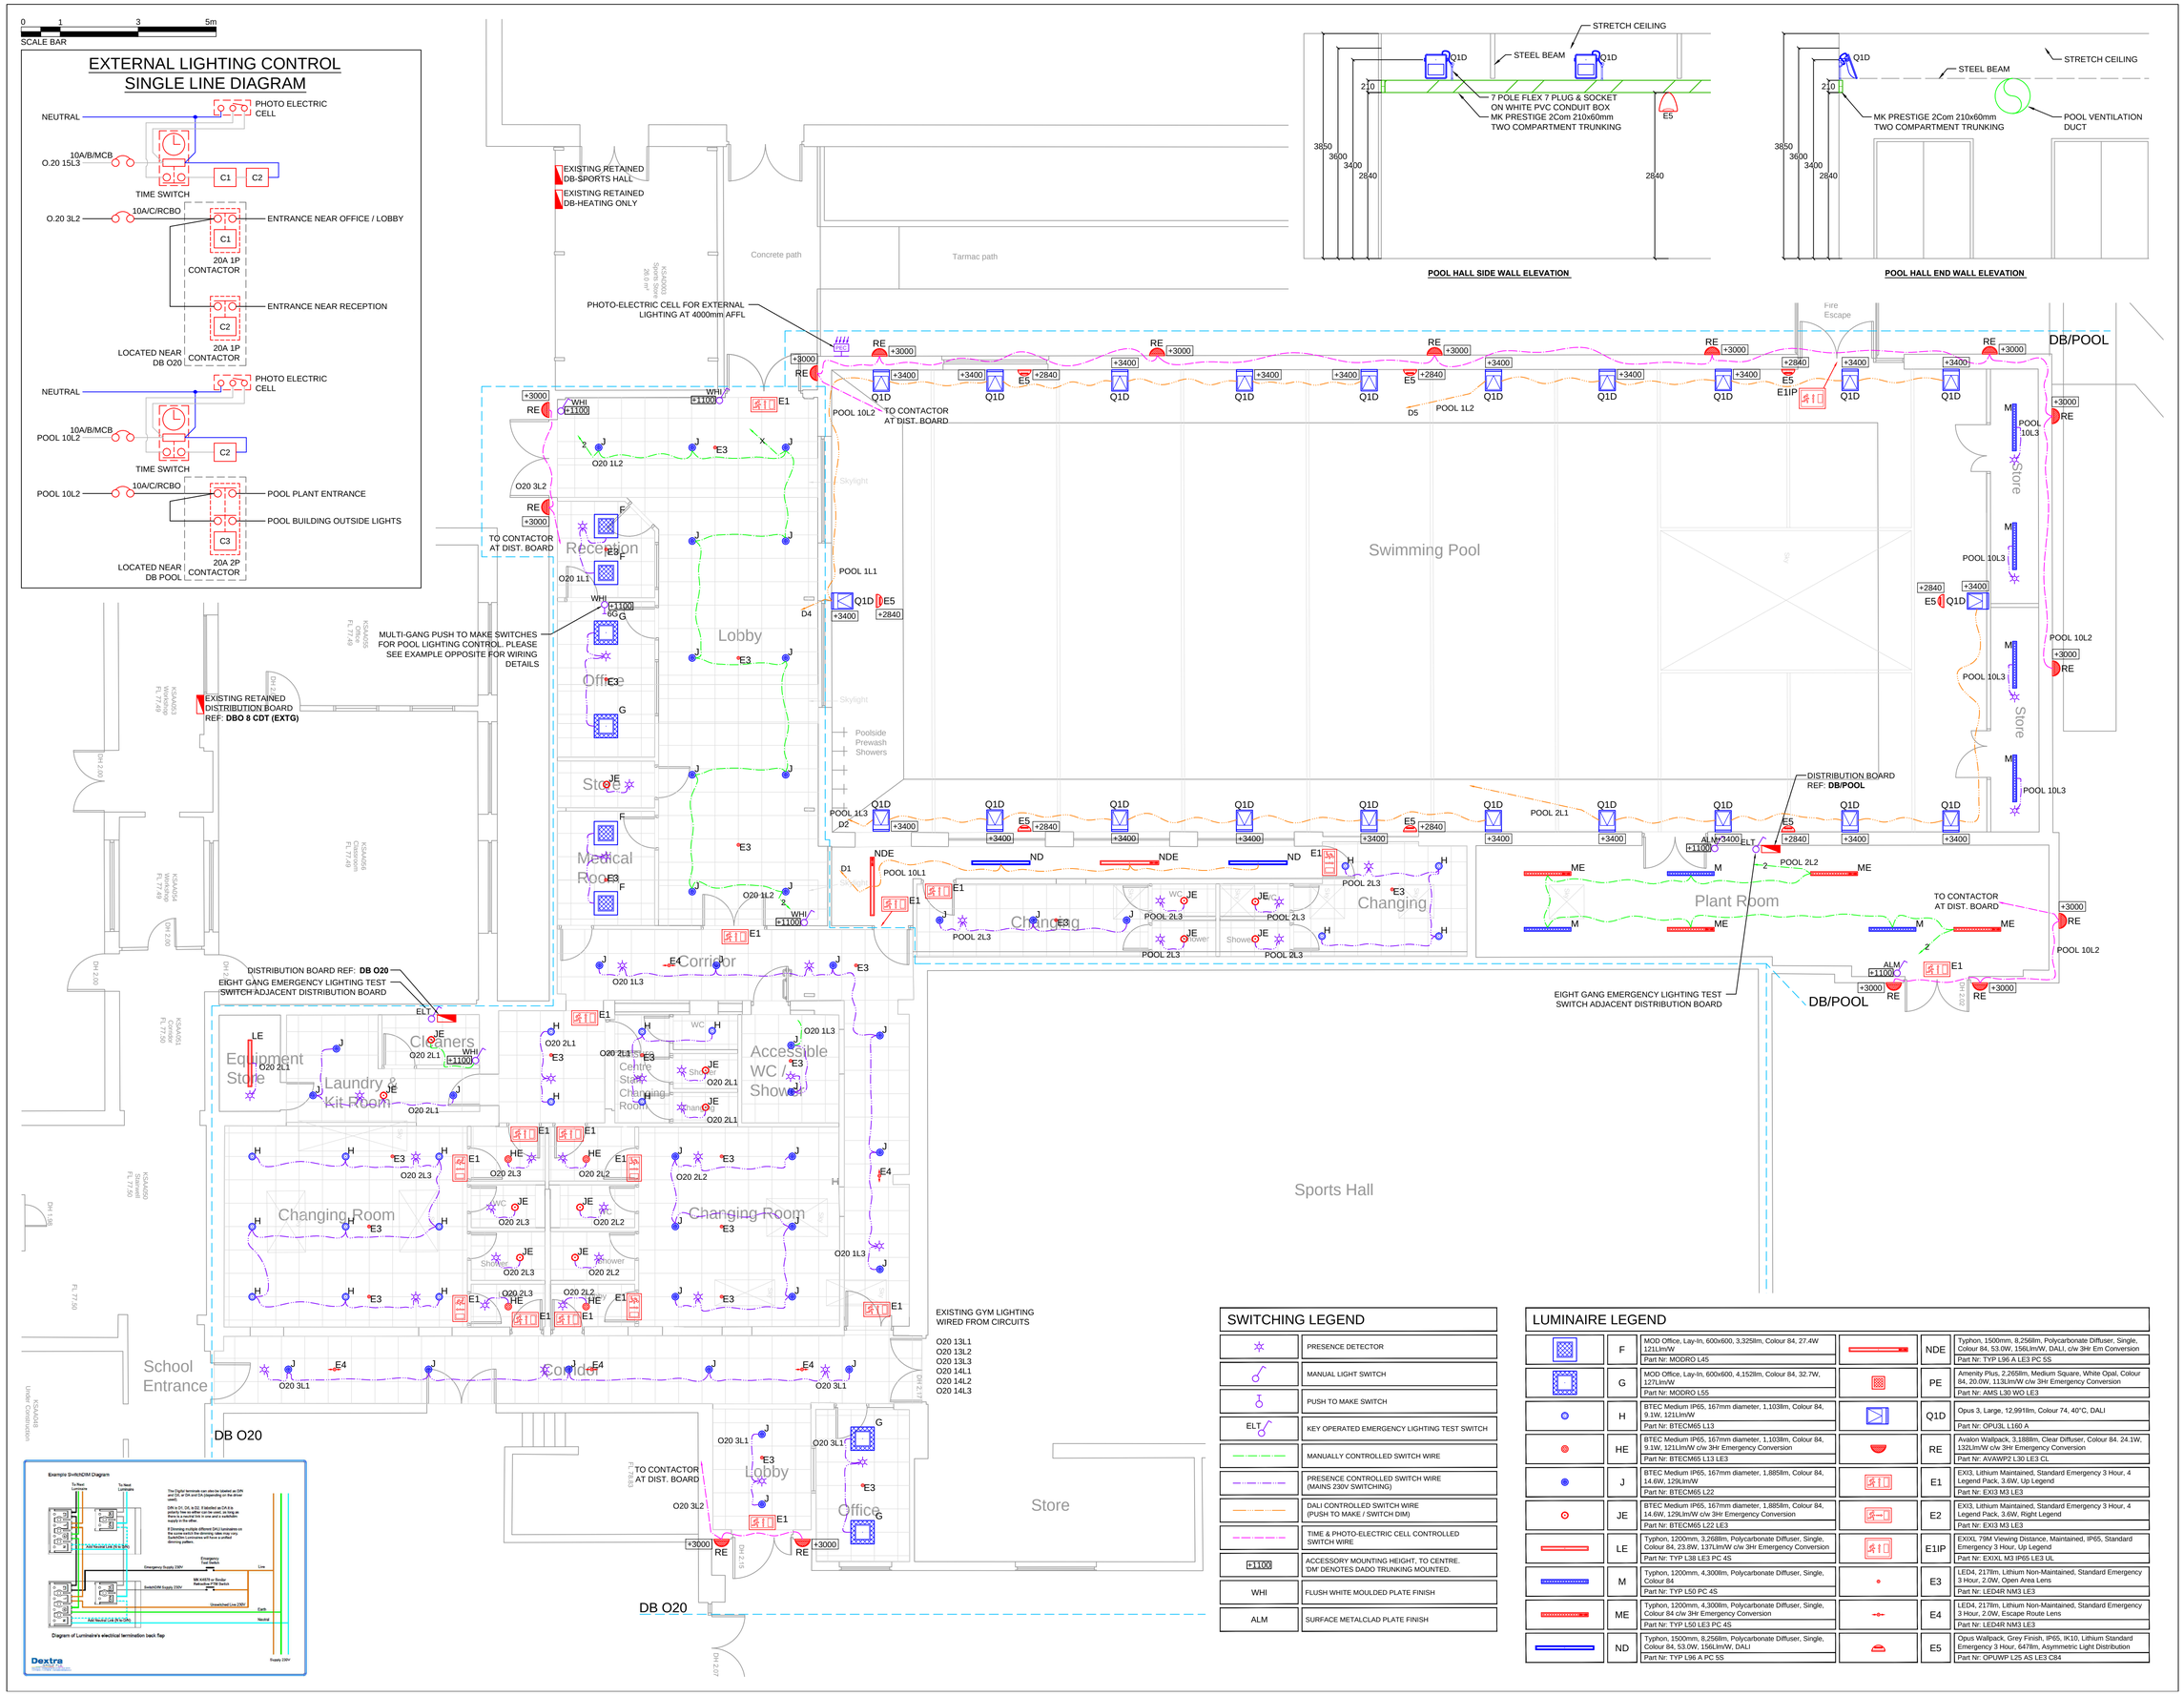

SWITCHING LEGEND

	PRESENCE DETECTOR
	MANUAL LIGHT SWITCH
	PUSH TO MAKE SWITCH
ELT	KEY OPERATED EMERGENCY LIGHTING TEST SWITCH
	MANUALLY CONTROLLED SWITCH WIRE
	PRESENCE CONTROLLED SWITCH WIRE (MAINS 230V SWITCHING)
	DALI CONTROLLED SWITCH WIRE (PUSH TO MAKE / SWITCH DIM)
	TIME & PHOTO-ELECTRIC CELL CONTROLLED SWITCH WIRE
+1100	ACCESSORY MOUNTING HEIGHT, TO CENTRE. 'DM' DENOTES DADO TRUNKING MOUNTED.
WHI	FLUSH WHITE MOULDED PLATE FINISH
ALM	SURFACE METALCLAD PLATE FINISH

LUMINAIRE LEGEND

	F	MOD Office, Lay-In, 600x600, 3,325lm, Colour 84, 27.4W 121Lm/W Part Nr: MODRO L45		NDE	Typhon, 1500mm, 8,256lm, Polycarbonate Diffuser, Single, Colour 84, 53.0W, 156Lm/W, DALI, c/w 3Hr Em Conversion Part Nr: TYP L96 A LE3 PC SS
	G	MOD Office, Lay-In, 600x600, 4,152lm, Colour 84, 32.7W, 127Lm/W Part Nr: MODRO L55		PE	Amenity Plus, 2,265lm, Medium Square, White Opal, Colour 84, 20.0W, 113Lm/W c/w 3Hr Emergency Conversion Part Nr: AMS L30 WO LE3
	H	BTEC Medium IP65, 167mm diameter, 1,103lm, Colour 84, 9.1W, 121Lm/W Part Nr: BTECM65 L13		Q1D	Opus 3, Large, 12,991lm, Colour 74, 40°C, DALI Part Nr: OPU3L L160 A
	HE	BTEC Medium IP65, 167mm diameter, 1,103lm, Colour 84, 9.1W, 121Lm/W c/w 3Hr Emergency Conversion Part Nr: BTECM65 L13 LE3		RE	Avalon Wallpack, 3,188lm, Clear Diffuser, Colour 84. 24.1W, 132Lm/W c/w 3Hr Emergency Conversion Part Nr: AVAWP2 L30 LE3 CL
	J	BTEC Medium IP65, 167mm diameter, 1,885lm, Colour 84, 14.6W, 129Lm/W Part Nr: BTECM65 L22		E1	EXI3, Lithium Maintained, Standard Emergency 3 Hour, 4 Legend Pack, 3.6W, Up Legend Part Nr: EXI3 M3 LE3
	JE	BTEC Medium IP65, 167mm diameter, 1,885lm, Colour 84, 14.6W, 129Lm/W c/w 3Hr Emergency Conversion Part Nr: BTECM65 L22 LE3		E2	EXI3, Lithium Maintained, Standard Emergency 3 Hour, 4 Legend Pack, 3.6W, Right Legend Part Nr: EXI3 M3 LE3
	LE	Typhon, 1200mm, 3,268lm, Polycarbonate Diffuser, Single, Colour 84, 23.8W, 137Lm/W c/w 3Hr Emergency Conversion Part Nr: TYP L38 LE3 PC AS		E1IP	EXIXL 79M Viewing Distance, Maintained, IP65, Standard Emergency 3 Hour, Up Legend Part Nr: EXIXL M3 IP65 LE3 UL
	M	Typhon, 1200mm, 4,300lm, Polycarbonate Diffuser, Single, Colour 84 Part Nr: TYP L50 PC AS		E3	LED4, 217lm, Lithium Non-Maintained, Standard Emergency 3 Hour, 2.0W, Open Area Lens Part Nr: LED4R NM3 LE3
	ME	Typhon, 1200mm, 4,300lm, Polycarbonate Diffuser, Single, Colour 84 c/w 3Hr Emergency Conversion Part Nr: TYP L50 LE3 PC AS		E4	LED4, 217lm, Lithium Non-Maintained, Standard Emergency 3 Hour, 2.0W, Escape Route Lens Part Nr: LED4R NM3 LE3
	ND	Typhon, 1500mm, 8,256lm, Polycarbonate Diffuser, Single, Colour 84, 53.0W, 156Lm/W, DALI Part Nr: TYP L96 A PC SS		E5	Opus Wallpack, Grey Finish, IP65, IK10, Lithium Standard Emergency 3 Hour, 647lm, Asymmetric Light Distribution Part Nr: OPUWP L25 AS LE3 C84

NOTES

ORIGINAL A1

DO NOT SCALE FROM THIS DRAWING.
IF IN DOUBT ASK.

AS FITTED DRAWING

Originator

Tec Electrical Services Ltd

Client

gleeds

Project

KINGSBURY SCHOOL SWIMMING POOL REFURBISHMENT

Title

GENERAL & EMERGENCY LIGHTING LAYOUT

Design	Drawn	Date
TEC	TEC	FEB '26

Scale: 1:75 @ A1

Background Drawing: NTBS4235 Kingsbury School 01-10-25

Drawing No.: E300

Rev: AF

Status: AS FITTED